


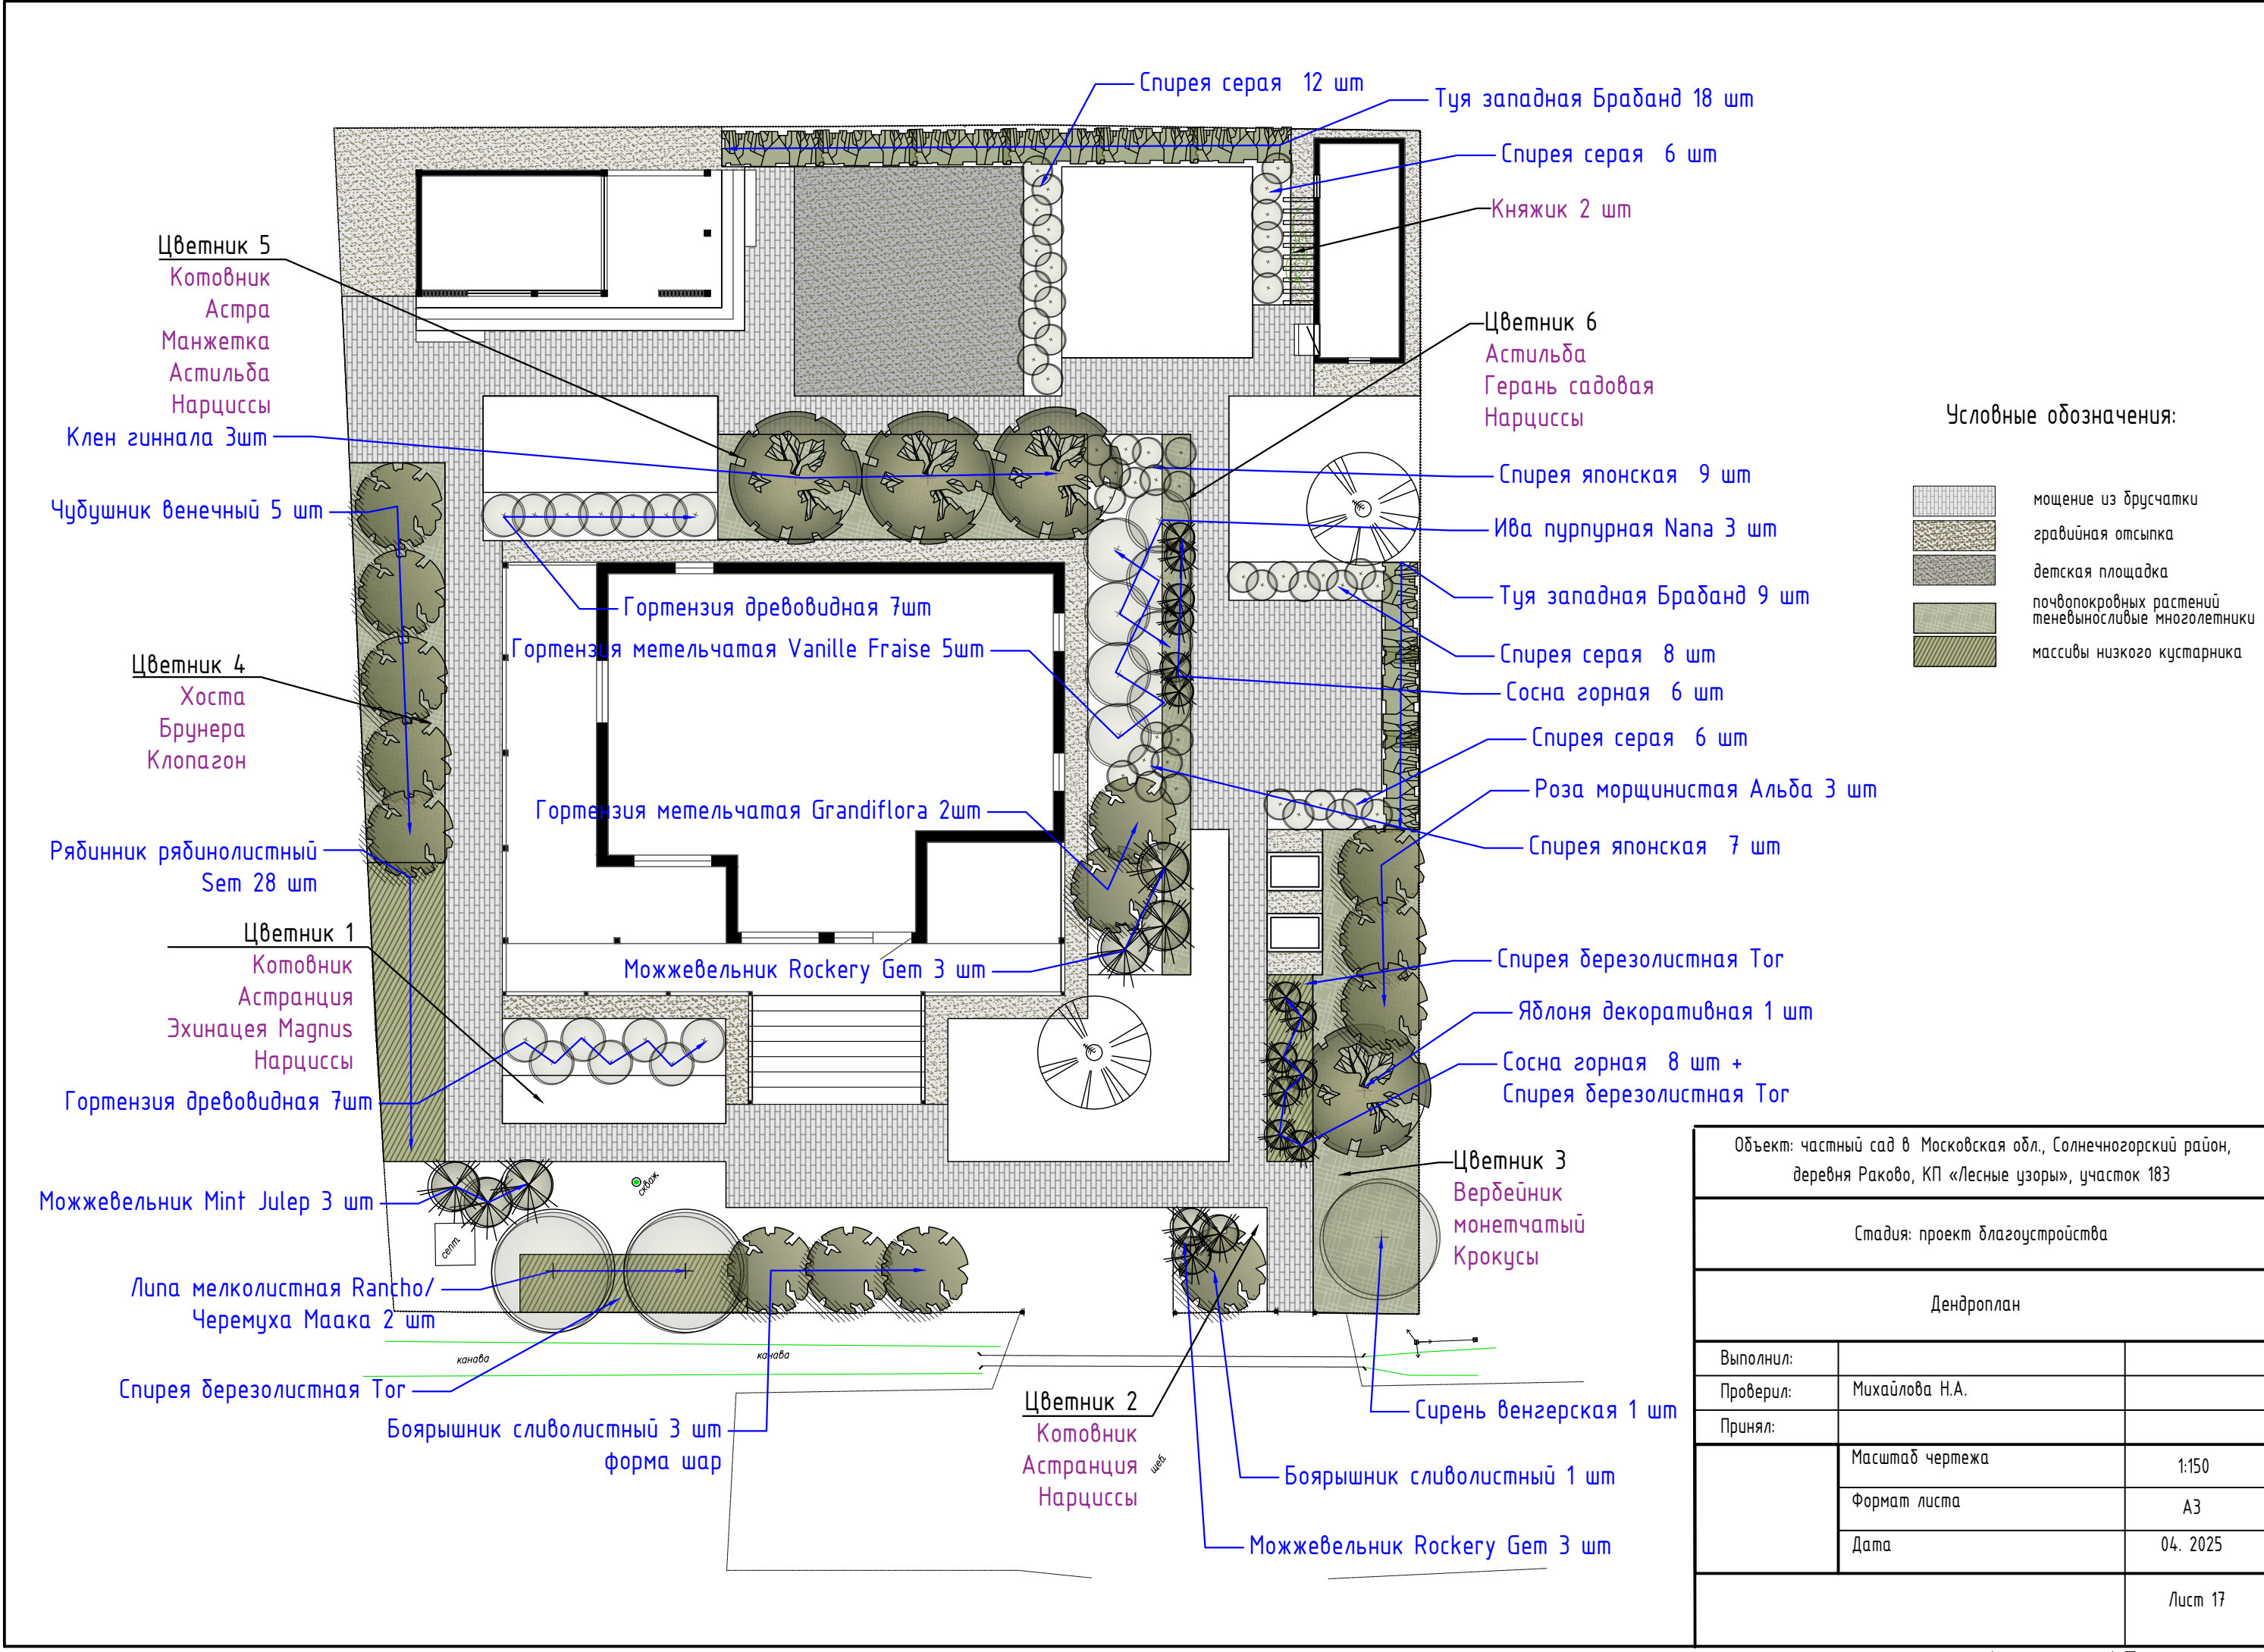

Условные обозначения:

- мощение из брусчатки
- гравийная отсыпка
- детская площадка
- почвопокровных растений
теневыносливые многолетники
- массивы низкого кустарника

Объект: частный сад в Московской обл., Солнечногорский район, деревня Раково, КП «Лесные узоры», участок 183		
Стадия: проект благоустройства		
Дендроплан		
Выполнил:		
Проверил:	Михайлова Н.А.	
Принял:		
	Масштаб чертежа	1:150
	Формат листа	A3
	Дата	04. 2025
		Лист 17