


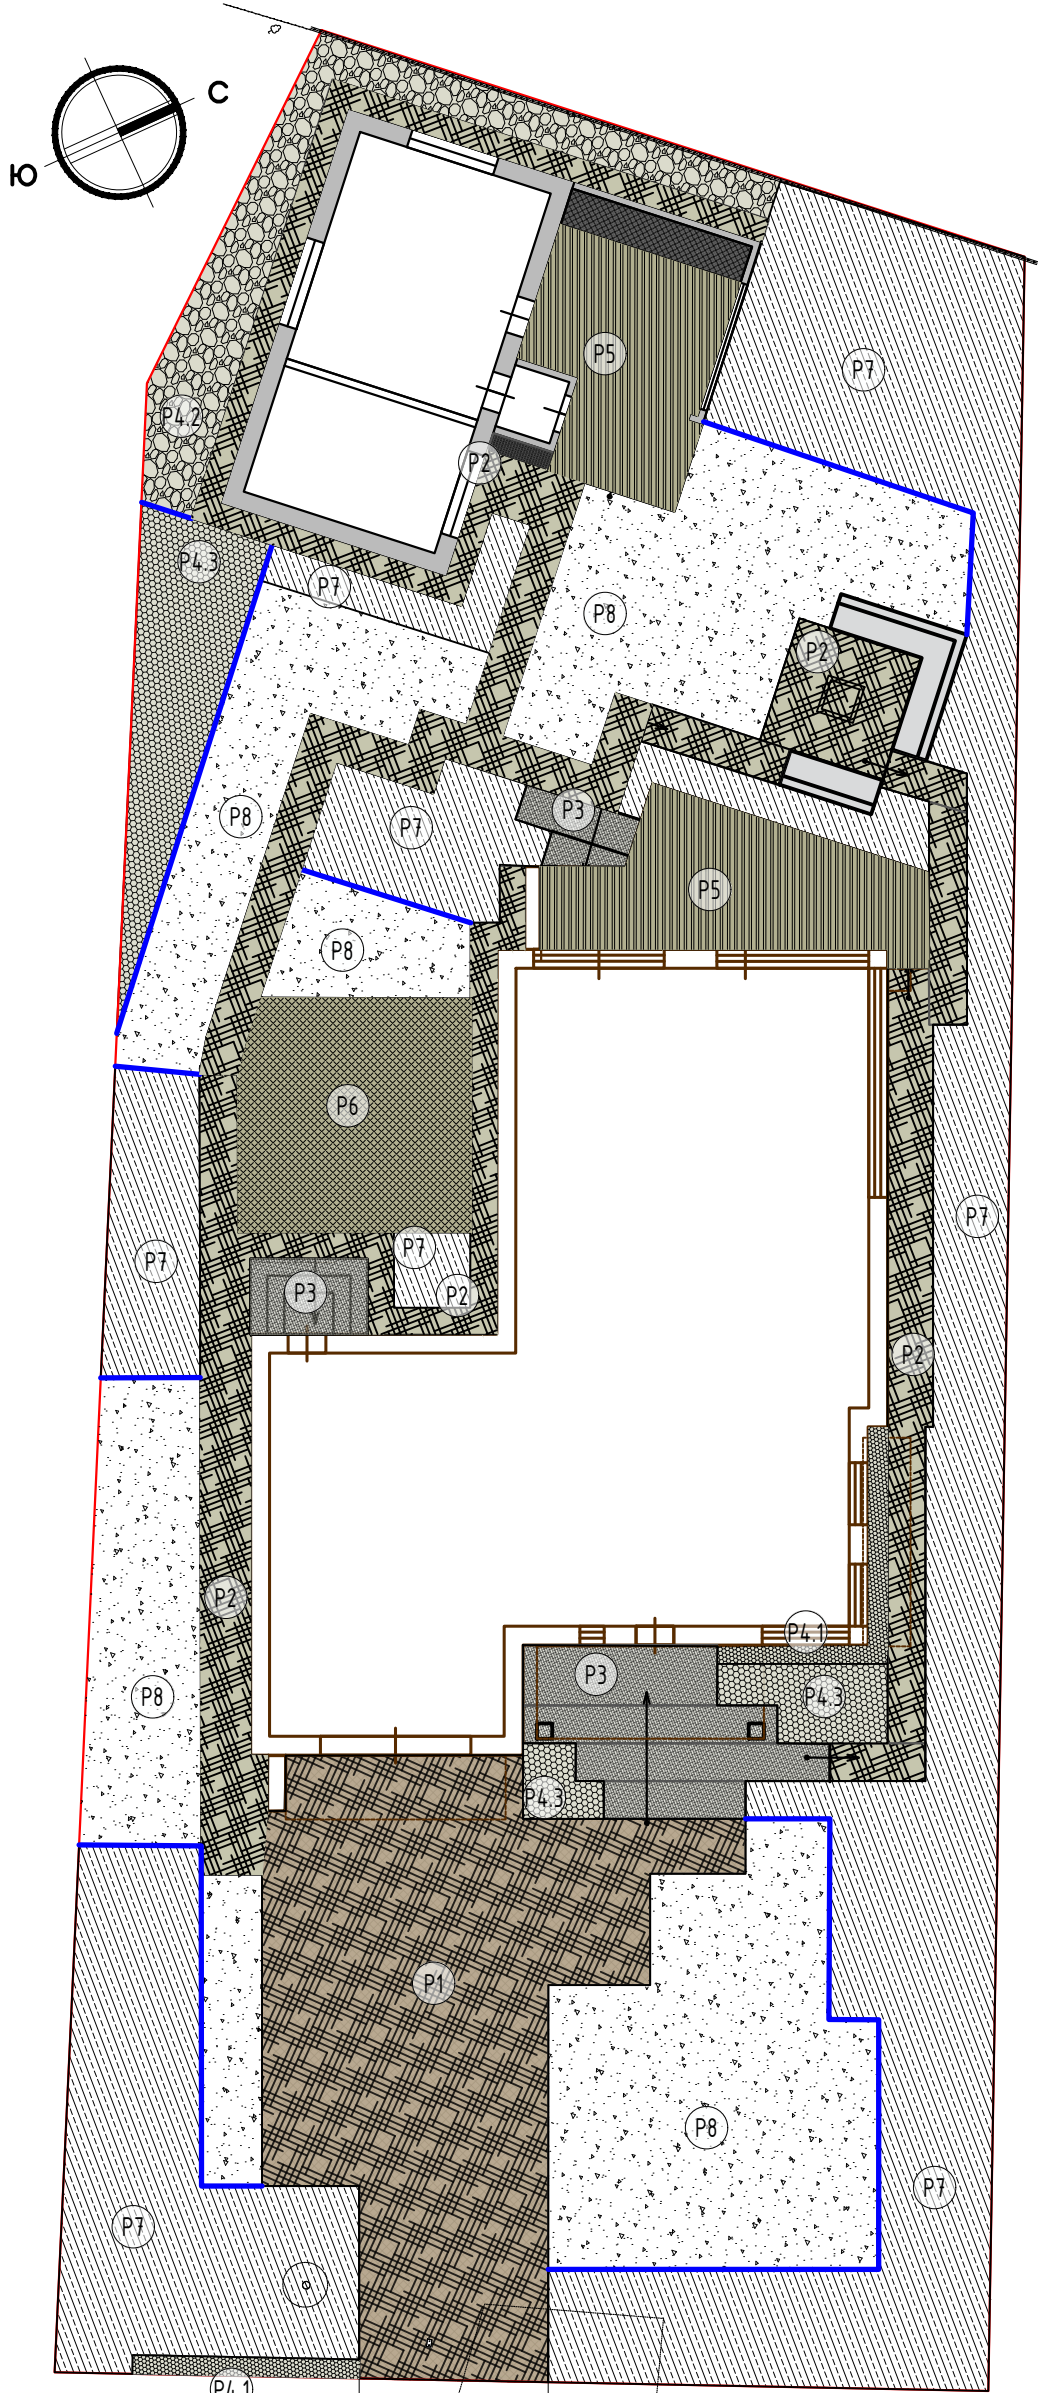

Ведомость тротуаров, дорожек и площадок

Поз.	Наименование	Тип	Площадь покрытия, м²	Примечание
1	Мощение плитами на твердом основании	P1	125.30	парковка
2	Мощение плитами на твердом основании	P2	140.90	дорожки, кострище, отмостка
3	Покрытие плитами на твердое основание	P3	36.00	лестница
4	Гравийное покрытие	P4.1	8.10	отмостка, основание под ворота
5	Гравийное покрытие	P4.2	33.30	зона за баней
6	Гравийное покрытие	P4.3	36.10	мульчирование под растениями
7	Деревянный настил	P5	58.80	терраса дома и бани
8	Резиновое покрытие	P6	37.70	детская площадка
9	Мульчирование миксбордеров	P7	327.40	зона внутренней территории
10	Газон	P8	247.50	рулонный
11	Борт из металлической полосы прямой	пог м	73.30	нержавеющая сталь/оцинкованная сталь

Условные обозначения:

- мощение брусчаткой (тип P1)
- мощение брусчаткой (тип P2)
- лестница (тип P3)
- гравийное покрытие (тип P4.1)
- гравийное покрытие (тип P4.2)
- гравийное покрытие (тип P4.3)
- деревянный настил (тип P5)
- резиновое покрытие (тип P6)
- мульчирование миксбордеров (тип P7)
- газон (тип P8)
- борт из металлической полосы прямой

Объект: частный сад Москва, пос. Первомайское, КП Староникольское

Стадия: проект благоустройства

План покрытий

Выполнил:		
Проверил:	Михайлова Н.А.	
Принял:		
	Масштаб чертежа	1:200
	Формат листа	A3
	Дата	06.2024
		Лист 14