


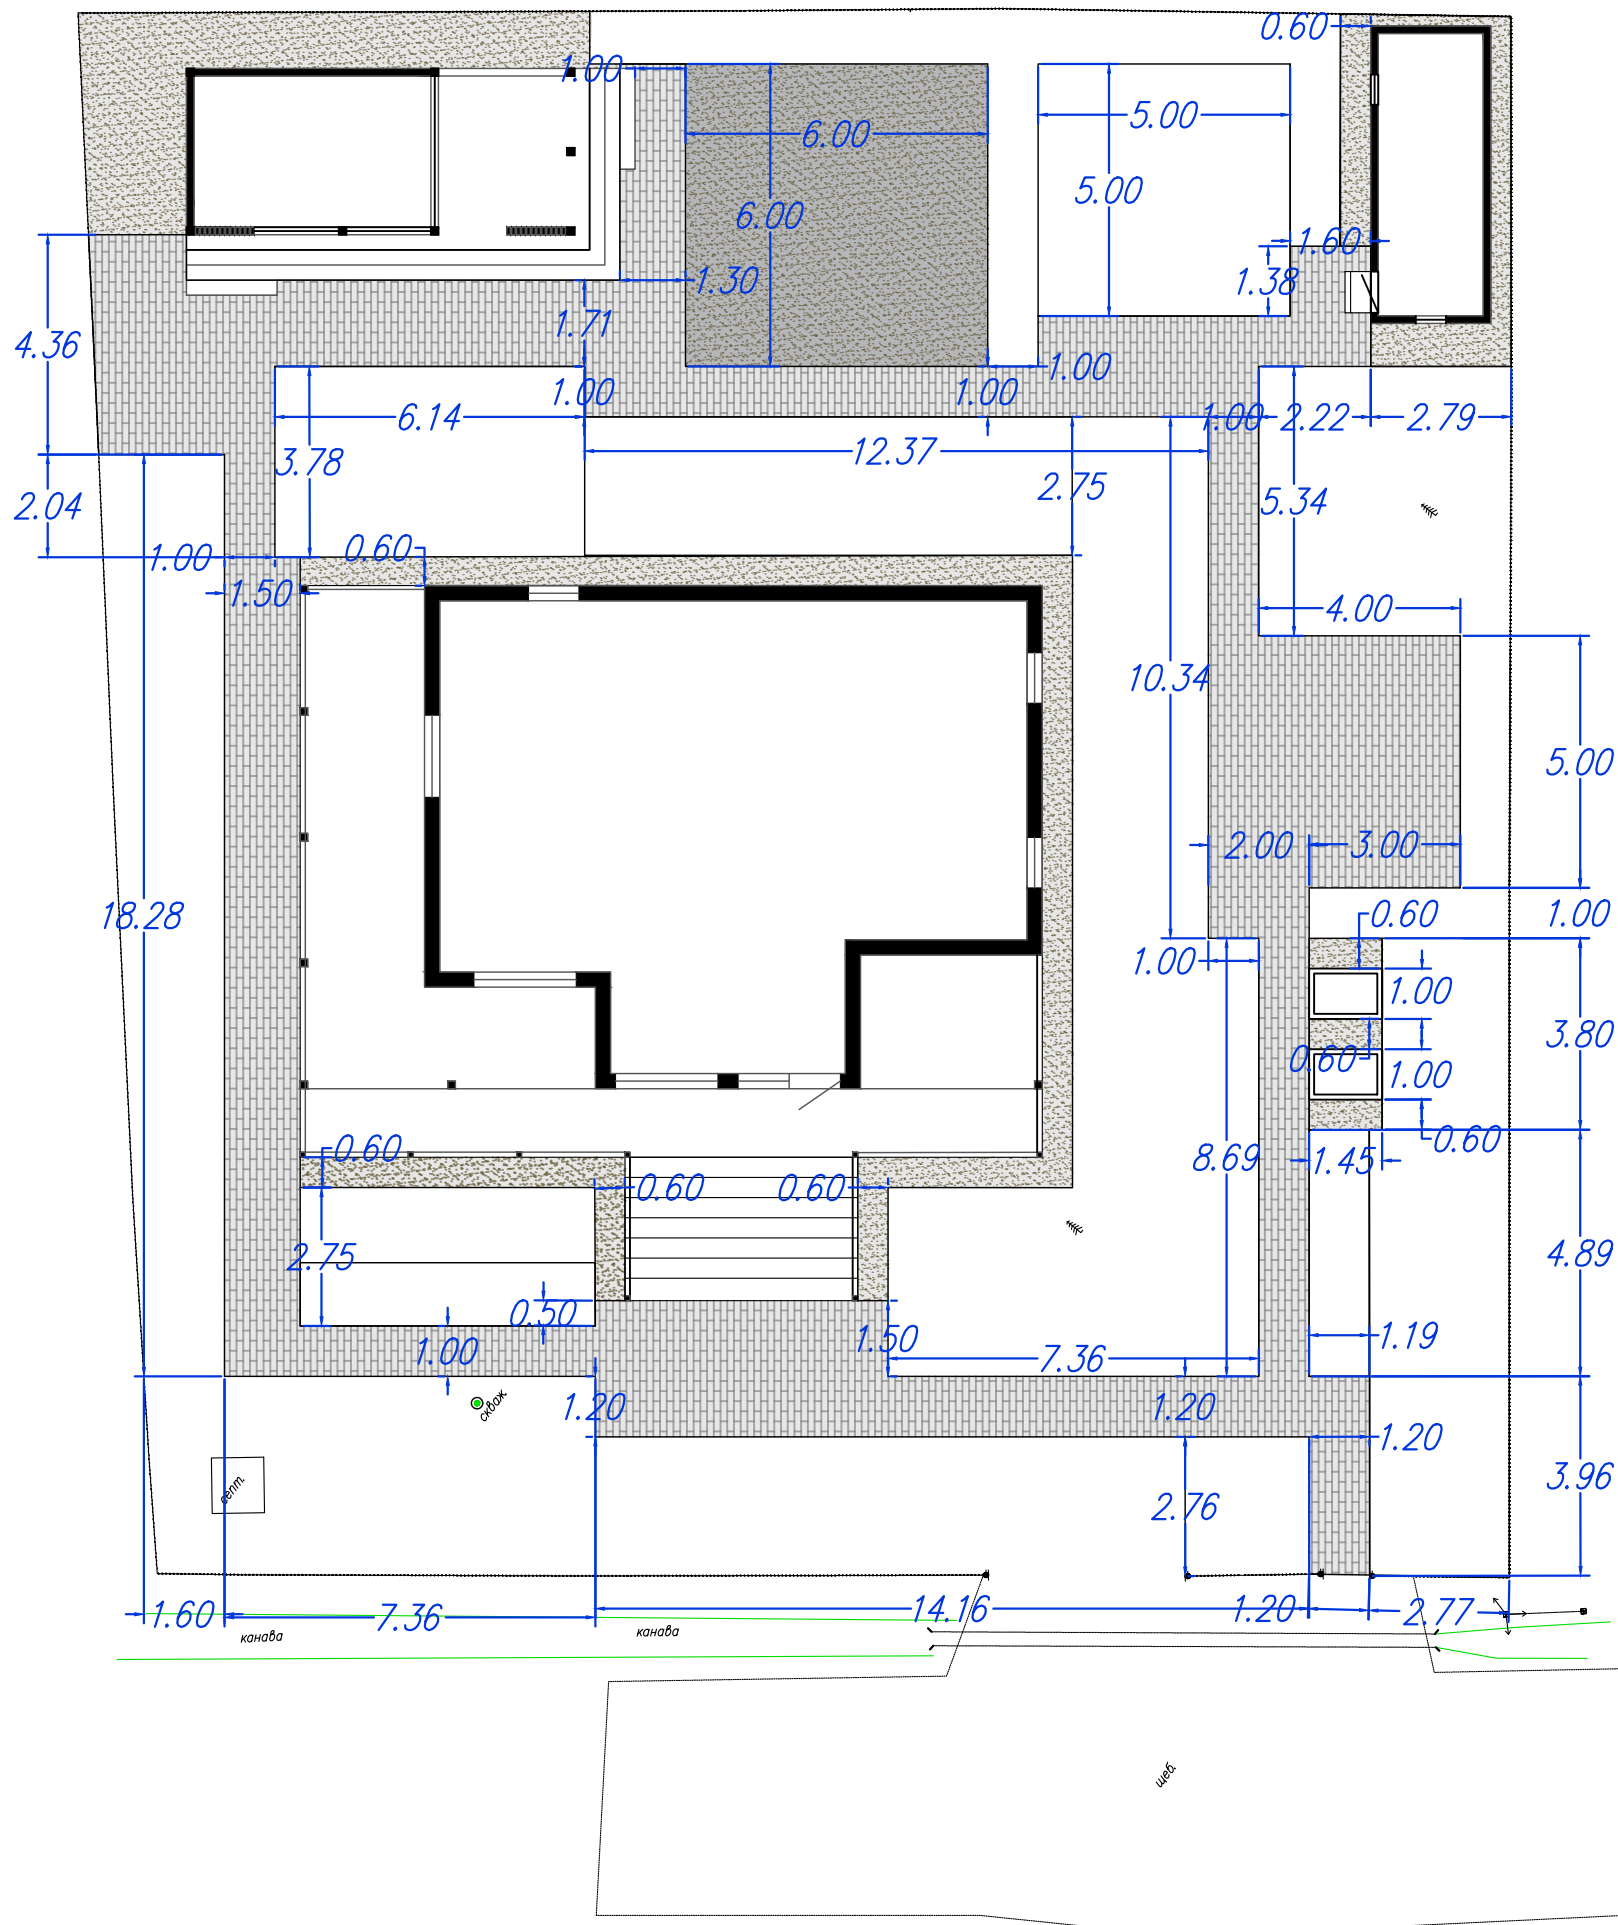

Объект: частный сад в Московской обл., Солнечногорский район, деревня Раково, КП «Лесные узоры», участок 183		
Стадия: проект благоустройства		
Разбивочный чертеж		
Выполнил:		
Проверил:	Михайлова Н.А.	
Принял:		
	Масштаб чертежа	1:150
	Формат листа	A3
	Дата	04. 2025
		Лист 13